SALEM HILLS HS FIELD HOUSE AV/TCU- NSD

AUDIOVISUAL SHOP DRAWINGS

MARSHALL INDUSTRIES • 3800 WEST 2100 SOUTH, SALT LAKE CITY, UT • 801.266.2428

TABLE OF CONTENTS

REV	DRAWING NUMBER	TITLE	DESCRIPTION	APP BY
		AV000 - GENERAL DRAWINGS		
	AV000	TABLE OF CONTENTS		
	AV001	AV LEGENDS AND KEYS	ROUGH-IN	
	AV002	AV LEGENDS AND KEYS	STRUCTURED CABLING	
		AV100 - WIREPATH AND BACKBOXES		
	AV100	TYPICAL AREAS		
	AV101	FIELD HOUSE		
		AV200 - REFLECTED CEILING		
	AV201	FIELD HOUSE		
		AV700 - PLATE DETAILS		
	AV701	UTILIZED PLATES		
		AV800 - SINGLE LINE DIAGRAMS		
	AV801.1	TYPICALCLASSROOM	SYSTEM FUNCTIONAL	
	AV802.1	FIELDHOUSE	SYSTEM FUNCTIONAL	
		AV900 - ENCLOSURE ELEVATIONS		
	AV901	UTILIZED RACKS		
		INTERCOMMUNICATION		
	IC101	MAIN LEVEL		
	IC102	SECOND LEVEL		
	IC801.1	GENERIC TCU RISER		

MARSHALL INDUSTRIES

www.marshallind.com

PROJECT INFORMATION

5795

SALEM HILLS HS

FIELD HOUSE AV/TCU- NSD

CUSTOMER NAME: NEBO UT SCHOOL DISTRICT	CUSTOMER NUMBER: 1699
SITE NAME: SALEM HILLS HIGH SCHOOL	SITE NUMBER: 122928

SITE ADDRESS: 200 NORTH MAIN STREET SALEM, UT 84653

SALES PERSON: MALISA TROUTWINE	ENGINEERED BY: MIKE PLATTNER
DRAFTER: ELI ANDERSON	PROJECT MANAGER: BRETT MELI

DRAWING SET INFORMATION

PHASE: CONSTRUCTION

PUBLISH DATE: 1/14/2026

PLOT SIZE: ARCH FULL BLEED E (36.00 X 48.00 INCHES)

PLOT SCALE: 1' = 1'-0"

APPROVED BY: ----

SHEET REVISION INFORMATION

REVISION: ----

REVISION DATE: ----

REVISION DESCRIPTION: ----

REVISION & ISSUE HISTORY

ISSUED FOR:	REV.	DATE:
---	---	---
---	---	---
SALEM HILLS HS

GENERAL DRAWINGS

TABLE OF CONTENTS

AV000

FILE NAME: AV000.DWG

ENCLOSURE LEGEND

SYM	DESCRIPTION	ELEVATION	QTY 1G	2G	3G	4G	5G	6G
COMMONLY USED WALL BOXES								
C#	GENERIC 3" DEEP BACKBOX. REFER TO # FOR GANG SIZE.	COUNTER HEIGHT	0	0	0	0	0	0
R#		RECEPTACLE HEIGHT	0	0	0	0	0	0
S#		SWITCH HEIGHT	0	0	0	0	0	0

SYM	TYPE	GANG	DESCRIPTION	ELEVATION	QTY
PROJECT SPECIFIC WALL BOXES					
A		1	3" DEEP BACKBOX	+72" AFF	0
B		1	3" DEEP BACKBOX	+240" AFF	0
D		0			0
E					
F					
G					
H					
I					
J					
K					
L					
M					
N					
O					
P					
Q					
T					
U					
V					
W					
X					

SYM	TYPE	GANG	DESCRIPTION	ELEVATION	QTY
CEILING BOXES					
A	LIGHTSPEED DRQ	0	SELEF ENCLOSED SPEAKER	FLUSH IN CEILING	0
B		0			0
C		0			0
D					
E					
F					
G					
H					
I					
J					
K					
L					
M					
TABLE BOXES					
A					
B					
C					
D					
E					
F					
G					
H					
I					
J					
K					
L					

SYM	TYPE	GANG	DESCRIPTION	ELEVATION	QTY
FLOOR BOXES					
A		1		FINISH FLOOR	0
B					
C					
D					
E					
F					
G					
H					
I					
J					
K					
L					
M					
EQUIPMENT RACKS					
A	MIDDLE ATLANTIC DWR-18-22PD	0	18RU WALL RACK		0
B	FSR CB-22+	0	2X2 CEILING RACK	FLUSH IN CEILING	0
C					
D					
E					
F					
G					
H					
I					
J					
K					
L					

AV100/AV200 WIRE PATH AND ENCLOSURE EXAMPLE

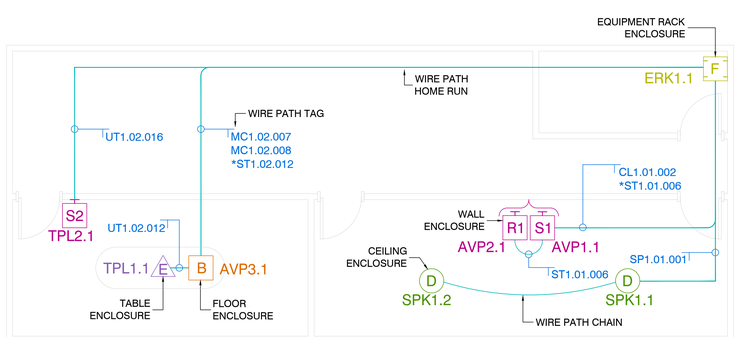

LOCATION EXAMPLE

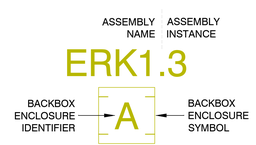

WIRE PATH TAG EXAMPLE

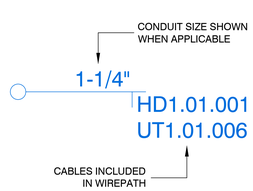

AV300 EQUIPMENT PLACEMENT EXAMPLE

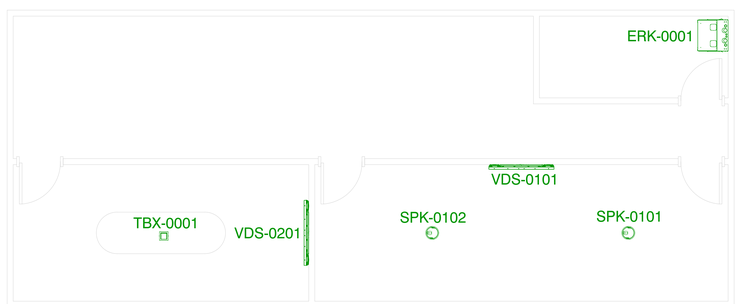

EQUIPMENT BLOCK EXAMPLE

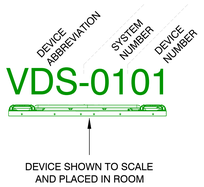

MARSHALL INDUSTRIES

www.marshallind.com

PROJECT INFORMATION

5795

SALEM HILLS HS

FIELD HOUSE AV/TCU- NSD

CUSTOMER NAME: NEBO UT SCHOOL DISTRICT	CUSTOMER NUMBER: 1699
SITE NAME: SALEM HILLS HIGH SCHOOL	SITE NUMBER: 122928
SITE ADDRESS: 200 NORTH MAIN STREET SALEM, UT 84653	
SALES PERSON: MALISA TROUTWINE	ENGINEERED BY: MIKE PLATTNER
DRAFTER: ELI ANDERSON	PROJECT MANAGER: BRETT MELI

DRAWING SET INFORMATION

PHASE: CONSTRUCTION

PUBLISH DATE: 1/14/2026

PLOT SIZE: ARCH FULL BLEED E (36.00 X 48.00 INCHES)

PLOT SCALE: 1' = 1'-0"

APPROVED BY: ----

SHEET REVISION INFORMATION

REVISION: ----

REVISION DATE: ----

REVISION DESCRIPTION: ----

REVISION & ISSUE HISTORY

ISSUED FOR:	REV.	DATE:
---	---	---
---	---	---
SALEM HILLS HS

GENERAL DRAWINGS

AV LEGENDS AND KEYS

ROUGH-IN

AV001

FILE NAME: AV000.DWG

ABRV.	DESCRIPTION
AAP	AMPLIFIED AUDIO PANEL
ACU	ACOUSTIC MATERIAL
ADC	AUDIO CONFERENCING
ALS	ASSISTED LISTENING SYSTEM
AMP	AMPLIFIER
AMS	ASSET MANAGEMENT
ANN	ANNOTATOR
ANT	ANTENNA
ARS	AUDIO RESPONSE SYSTEM
ASP	AUDIO SIGNAL PROCESSOR
AVF	AUDIO/VIDEO FURNITURE
AVL	AUDIO/VIDEO LIFT
AVP	AUDIO/VIDEO PANEL
AVT	AUDIO/VIDEO PANEL
BAG	EQUIPMENT BAG
BGM	BACKGROUND MUSIC SYSTEM
BOB	BREAK OUT BOX
CAM	CAMERA
CBX	CEILING BOX
CCU	CAMERA CONTROL UNIT
CLK	CLOCK
CNT	CONTROLLER
CNV	CONVERTER
COD	ENCODER/DECODER
CPU	COMPUTER
CRD	CARD/MODULE/INSERT
DAR	DIGITAL AUDIO RECORDER
DMP	DIGITAL MEDIA PLAYER
DMR	DIGITAL MEDIA RECORDER
DMT	DIGITAL MEDIA TRANSMISSION
DOC	DOCUMENT CAMERA
DSP	DIGITAL SIGNAGE SYSTEM
DTP	DISTANCE TRANSPORT
DVR	DIGITAL VIDEO RECORDER
DWR	DRAWER
EFX	EFFECTS PROCESSOR
EMI	IR/RF EMITTER
ENC	CHASSIS/CARD ENCLOSURE
ERK	EQUIPMENT RACK
FAN	FAN
FBX	FLOOR BOX
GUI	GRAPHICAL USER INTERFACE
ICS	INTERCOM SYSTEM
IFB	INTERUPTED FOLDBACK
INT	INTERFACE
IWB	WHITE BOARD
KPD	KEYPAD CONTROL
LEN	LENS
LGT	LIGHTING SYSTEM
MDI	MIDI CONTROLLER
MIC	MICROPHONE
MIX	MIXER
MOD	MODULATOR/DEMODULATOR
MON	MONITOR
MSG	MESSAGING SYSTEMS
MSK	SOUND MASKING SYSTEM
MTR	MAGNETIC TAPE RECORDER
NCS	NURSE CALL SYSTEM
NMD	NETWORK MEDIA DEVICE
NVR	NETWORK VIDEO RECORDER
NWD	NETWORK DEVICE
ODR	OPTICAL DISK RECORDER
PAS	PUBLIC ADDRESS SYSTEM
PGS	PAGING SYSTEM

ABRV.	DESCRIPTION
PPL	PATCH PANEL
PRJ	PROJECTOR
PWR	POWER DEVICE
REM	REMOTE CONTROL
RMK	RACK MOUNT KIT
ROB	ROBOTIC SYSTEM
RTS	DISCUSSION SYSTEM
SBX	STAGE BOX/SNAKE
SCN	PROJECTION SCREEN
SCR	SCALER/SCAN CONVERTER
SNS	SENSOR DEVICE
SOF	SOFTWARE
SPK	SPEAKER
SPT	RF SPLITTER
SWT	SWITCHER
TBX	TABLE BOX
TEL	TELEPHONES
TMP	TAPE MEDIA PLAYER
TPL	TOUCH PANEL
TRX	TRANSMITTER/RECIEVER
UPS	UNINTERRUPTABLE POWER SUPPLY
VDC	VIDEO CONFERENCING
VDS	VIDEO DISPLAY
VSP	VIDEO SIGNAL PROCESSOR
VWS	VIDEO WALL SYSTEM
WAP	WIRELESS ACCESS POINT
WBX	WALL BOX
WMR	WIRELESS TX/RX
XDA	DISTRIBUTION AMPLIFIER
XMR	TRANSFORMER
XXX	UNKNOWN

CABLE LEGEND

ID	MAKE	MODEL	DESCRIPTION	PLENUM
CONTROL CABLE TYPES				
CL1				
CL2				
CL3				
CL4				
CL5				
COAX CABLE TYPES				
CX1				
CX2				
CX3				
CX4				
CX5				
FIBER OPTIC CABLE TYPES				
FB1				
FB2				
FB3				
FB4				
HDMI CABLE TYPES				
HD1			PREMADE 3' HDMI CABLE	
HD2			PREMADE 6' HDMI CABLE	
HD3			PREMADE 10' HDMI CABLE	
HD4			PREMADE 15' HDMI CABLE	
HD5			PREMADE 30' HDMI CABLE	
HD6				
HD7				
HD8				
MICROPHONE AND LINE LEVEL AUDIO CABLE TYPES				
MC1				
MC2				
MC3				
MC4				
MC5				
MULTI-FUNCTION CABLE TYPES				
MF1				
MF2				
MF3				
MF4				
POWER CABLE TYPES				
PW1				
PW2				
PW3				
PW4				
PW5				
SPECIAL CABLE TYPES				
SL1				
SL2				
SL3				
SL4				
SPEAKER CABLE TYPES				
SP1				
SP2				
SP3				
SP4				
SP5				
SHIELDED TWISTED PAIR CABLE TYPES				
ST1				
ST2				
ST3				
ST4				
ST5				
USB CABLE TYPES				
US1				
US2				
US3				
US4				
US5				
UNSHIELDED TWISTED PAIR CABLE TYPES				
UT1				
UT2				
UT3				
UT4				
UT5				

AV800 SINGLE LINE DIAGRAM EXAMPLE

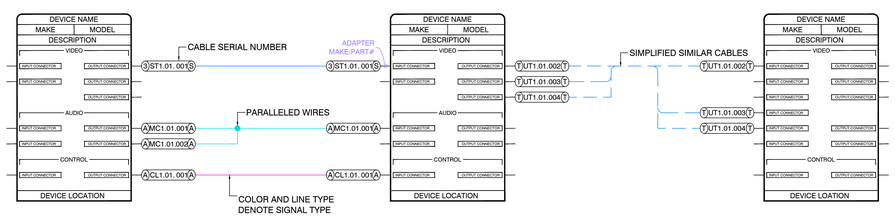

AV800 CABLE SERIAL NUMBER EXAMPLE

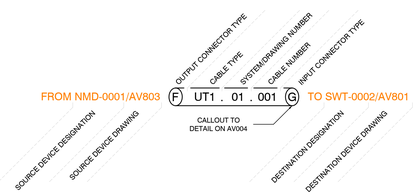

LINE DESIGNATIONS KEY

- BULK - AUDIO
- PATCH - AUDIO
- BULK - VIDEO
- PATCH - VIDEO
- BULK - CONTROL
- PATCH - CONTROL
- BULK - GENERIC
- PATCH - GENERIC

MARSHALL INDUSTRIES

www.marshallind.com

PROJECT INFORMATION

5795

SALEM HILLS HS

FIELD HOUSE AV/TCU- NSD

CUSTOMER NAME: NEBO UT SCHOOL DISTRICT	CUSTOMER NUMBER: 1699
SITE NAME: SALEM HILLS HIGH SCHOOL	SITE NUMBER: 122928
SITE ADDRESS: 200 NORTH MAIN STREET SALEM, UT 84653	
SALES PERSON: MALISA TROUTWINE	ENGINEERED BY: MIKE PLATTNER
DRAFTER: ELI ANDERSON	PROJECT MANAGER: BRETT MELI

DRAWING SET INFORMATION

PHASE: CONSTRUCTION

PUBLISH DATE: 1/14/2026

PLOT SIZE: ARCH FULL BLEED E (36.00 X 48.00 INCHES)

PLOT SCALE: 1' = 1'-0"

APPROVED BY: ----

SHEET REVISION INFORMATION

REVISION: ---- REVISION DATE: ---- REVISION DESCRIPTION: ----

REVISION & ISSUE HISTORY

ISSUED FOR:	REV.	DATE:
---	---	---
---	---	---
SALEM HILLS HS

GENERAL DRAWINGS

AV LEGENDS AND KEYS

STRUCTURED CABLING

AV002

FILE NAME: AV000.DWG

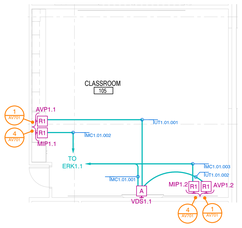

1 **TYPICAL CLASSROOM - PLAN**
SCALE: 1/8" = 1'-0"

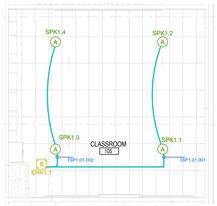

2 **TYPICAL CLASSROOM - RCP**
SCALE: 1/8" = 1'-0"

MARSHALL
INDUSTRIES

www.marshallind.com

PROJECT INFORMATION

5795

SALEM HILLS HS

FIELD HOUSE AV/TCU- NSD

CUSTOMER NAME: NEBO UT SCHOOL DISTRICT	CUSTOMER NUMBER: 1699
SITE NAME: SALEM HILLS HIGH SCHOOL	SITE NUMBER: 122928
SITE ADDRESS: 200 NORTH MAIN STREET SALEM, UT 84653	
SALES PERSON: MALISA TROUTWINE	ENGINEERED BY: MIKE PLATTNER
DRAFTER: ELI ANDERSON	PROJECT MANAGER: BRETT MELI

DRAWING SET INFORMATION

PHASE: CONSTRUCTION

PUBLISH DATE: 1/14/2026

PLOT SIZE: ARCH FULL BLEED E (36.00 X 48.00 INCHES)

PLOT SCALE: 1' = 1'-0"

APPROVED BY: -----

SHEET REVISION INFORMATION

REVISION:	REVISION DATE:	REVISION DESCRIPTION:
----	----	----

REVISION & ISSUE HISTORY

ISSUED FOR:	REV.	DATE:
---	---	---
---	---	---
SALEM HILLS HS

WIREPATH AND BACKBOXES

TYPICAL AREAS

AV100

FILE NAME: AV100.DWG

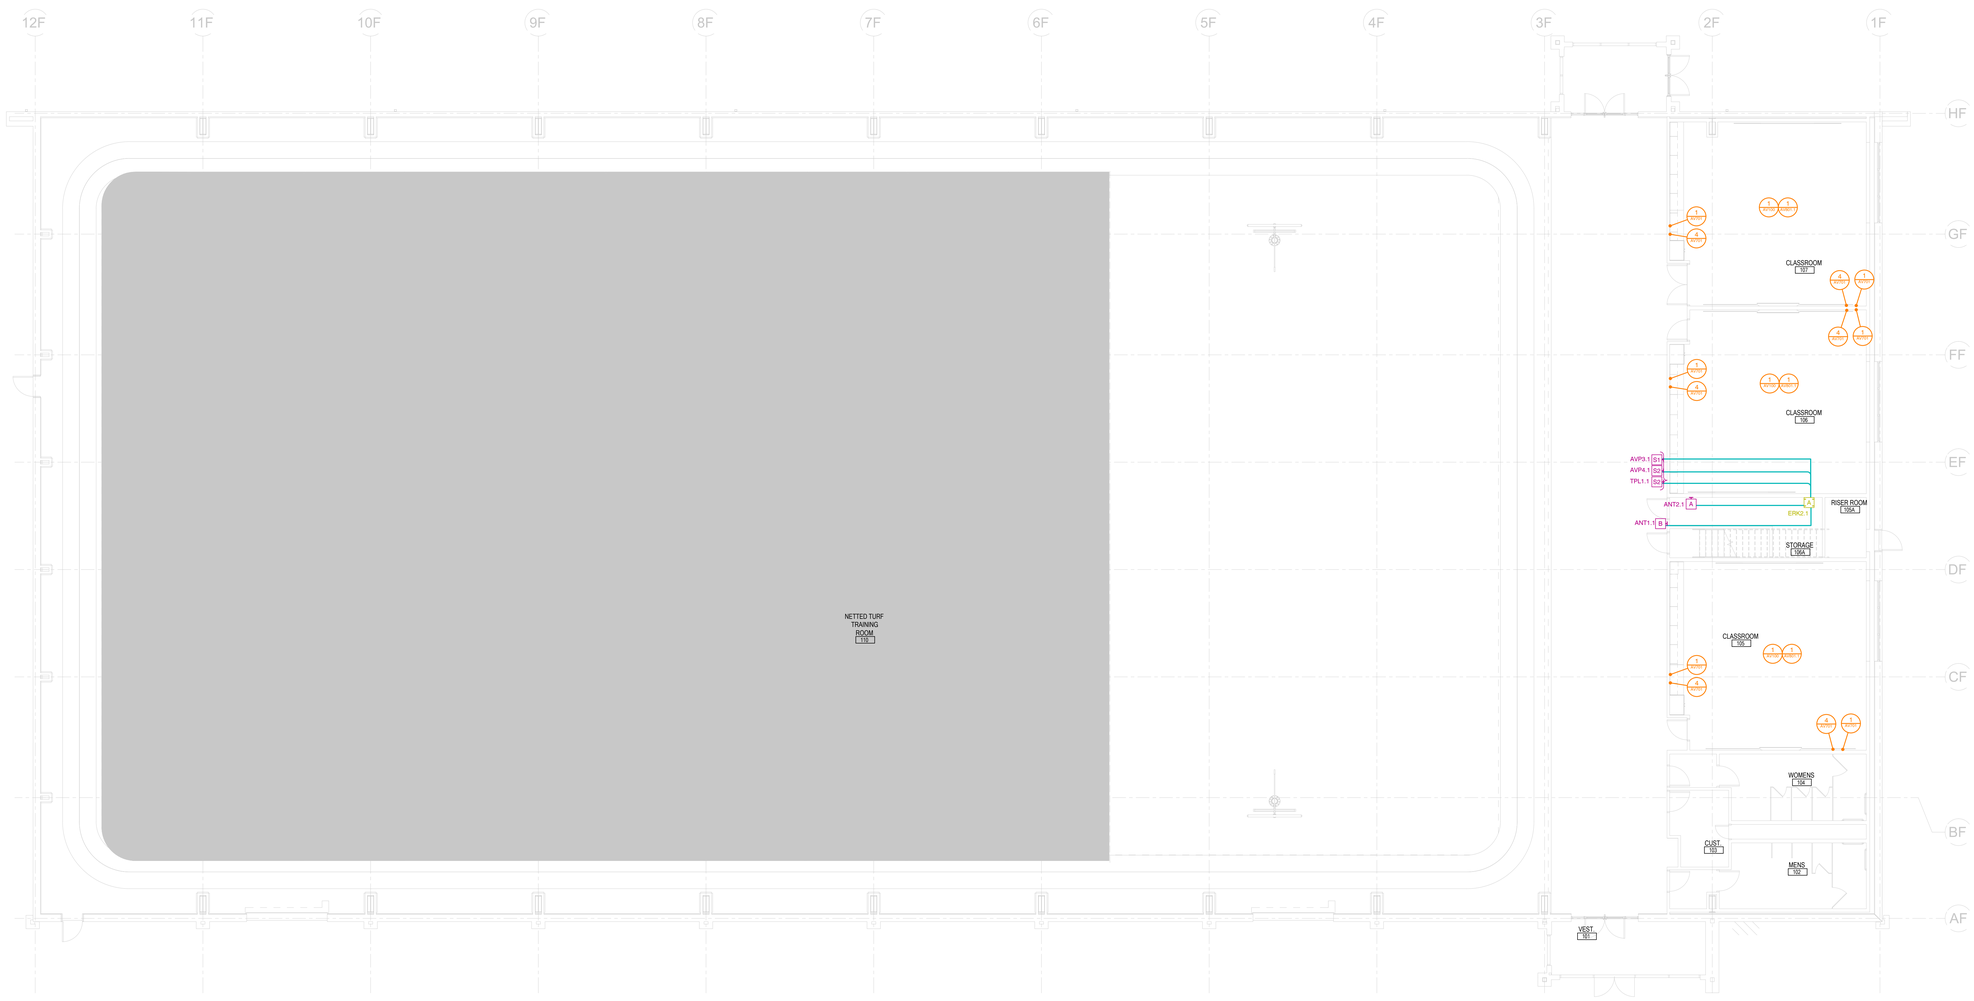

MARSHALL INDUSTRIES

www.marshallind.com

PROJECT INFORMATION

5795

SALEM HILLS HS

FIELD HOUSE AV/TCU- NSD

CUSTOMER NAME: NEBO UT SCHOOL DISTRICT	CUSTOMER NUMBER: 1699
SITE NAME: SALEM HILLS HIGH SCHOOL	SITE NUMBER: 122928
SITE ADDRESS: 200 NORTH MAIN STREET SALEM, UT 84653	
SALES PERSON: MALISA TROUTWINE	ENGINEERED BY: MIKE PLATTNER
DRAFTER: ELI ANDERSON	PROJECT MANAGER: BRETT MELI

DRAWING SET INFORMATION

PHASE: CONSTRUCTION

PUBLISH DATE: 1/14/2026

PLOT SIZE: ARCH FULL BLEED E (36.00 X 48.00 INCHES)

PLOT SCALE: 1' = 1'-0"

APPROVED BY: -----

SHEET REVISION INFORMATION

REVISION:	REVISION DATE:	REVISION DESCRIPTION:
----	----	----

REVISION & ISSUE HISTORY

ISSUED FOR:	REV.	DATE:
---	---	---
---	---	---
SALEM HILLS HS

WIREPATH AND BACKBOXES

FIELD HOUSE

AV101

FILE NAME: AV100.DWG

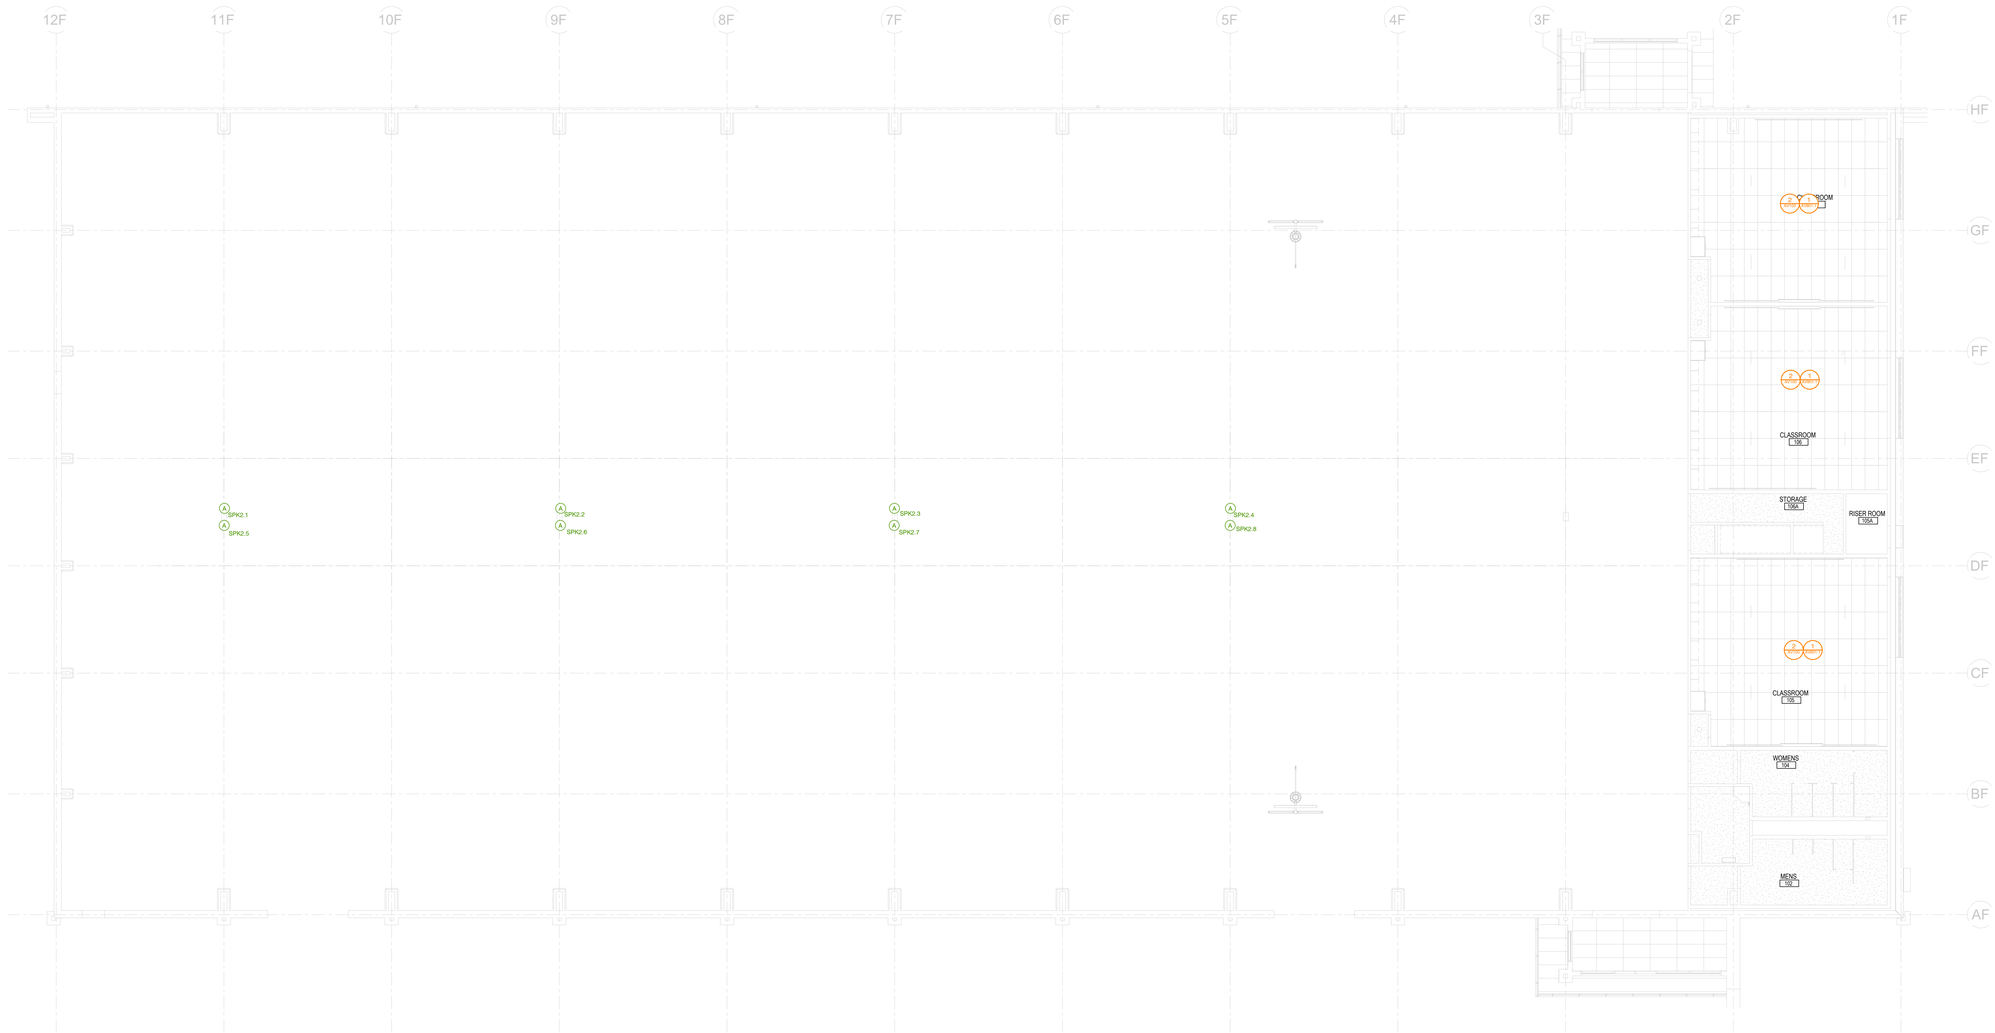

1 **FIELD HOUSE - RCP**
SCALE: 1/8" = 1'-0"

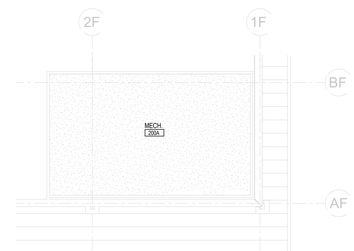

2 **SECOND LEVEL - MECH ROOM**
SCALE: 1/8" = 1'-0"

MARSHALL INDUSTRIES

www.marshallind.com

PROJECT INFORMATION

5795

SALEM HILLS HS

FIELD HOUSE AV/TCU- NSD

CUSTOMER NAME: NEBO UT SCHOOL DISTRICT	CUSTOMER NUMBER: 1699
SITE NAME: SALEM HILLS HIGH SCHOOL	SITE NUMBER: 122928

SITE ADDRESS:
200 NORTH MAIN STREET
SALEM, UT 84653

SALES PERSON: MALISA TROUTWINE	ENGINEERED BY: MIKE PLATTNER
DRAFTER: ELI ANDERSON	PROJECT MANAGER: BRETT MELI

DRAWING SET INFORMATION

PHASE: CONSTRUCTION

PUBLISH DATE: 1/14/2026

PLOT SIZE: ARCH FULL BLEED E (36.00 X 48.00 INCHES)

PLOT SCALE: 1' = 1'-0"

APPROVED BY: -----

SHEET REVISION INFORMATION

REVISION:	REVISION DATE:	REVISION DESCRIPTION:
----	----	----

REVISION & ISSUE HISTORY

ISSUED FOR:	REV.	DATE:
---	---	---
---	---	---
SALEM HILLS HS

REFLECTED CEILING

FIELD HOUSE

AV201

FILE NAME: AV100.DWG

DESIGNATION	DESCRIPTION	LOCATION
TRX-0101	HDMI TX	AVP1.1
TRX-0103	HDMI TX	AVP1.2

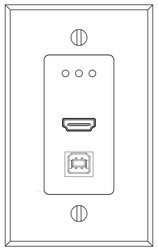

1 **AVP1**
HALL RESEARCH DSCV1-70-TX
SCALE: 1' = 1'-0"

DESIGNATION	DESCRIPTION	LOCATION
AVP-0201	NETWORK AUDIO INTERFACE	AVP3.1

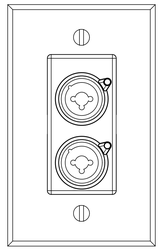

2 **AVP3**
QSC AXON D2I
SCALE: 1' = 1'-0"

DESIGNATION	DESCRIPTION	LOCATION
AVP-0202	BLUETOOTH DANTE WALLPLATE	AVP4.1

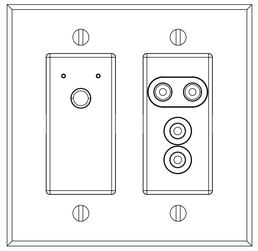

3 **AVP4**
QSC UND6IO-BT
SCALE: 1' = 1'-0"

DESIGNATION	DESCRIPTION	LOCATION
AVP-0101	AUX AUDIO PLATE	MIP1.1
AVP-0102	AUX AUDIO PLATE	MIP1.2

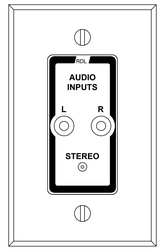

4 **MIP1**
RDL D-CIU3
SCALE: 1' = 1'-0"

DESIGNATION	DESCRIPTION	LOCATION
TPL-0201	TOUCH PANEL	TPL1.1

5 **TPL1**
QSC TSC-70-G3
SCALE: 1' = 1'-0"

MARSHALL INDUSTRIES

www.marshallind.com

PROJECT INFORMATION

5795

SALEM HILLS HS

FIELD HOUSE AV/TCU- NSD

CUSTOMER NAME: NEBO UT SCHOOL DISTRICT	CUSTOMER NUMBER: 1699
SITE NAME: SALEM HILLS HIGH SCHOOL	SITE NUMBER: 122928
SITE ADDRESS: 200 NORTH MAIN STREET SALEM, UT 84653	
SALES PERSON: MALISA TROUTWINE	ENGINEERED BY: MIKE PLATTNER
DRAFTER: ELI ANDERSON	PROJECT MANAGER: BRETT MELI

DRAWING SET INFORMATION

PHASE: CONSTRUCTION

PUBLISH DATE: 1/14/2026

PLOT SIZE: ARCH FULL BLEED E (36.00 X 48.00 INCHES)

PLOT SCALE: 1' = 1'-0"

APPROVED BY: ----

SHEET REVISION INFORMATION

REVISION:	REVISION DATE:
----	REVISION DESCRIPTION: ----

REVISION & ISSUE HISTORY

ISSUED FOR:	REV.	DATE:
---	---	---
---	---	---
SALEM HILLS HS

PLATE DETAILS

UTILIZED PLATES

AV701

FILE NAME: AV700.DWG

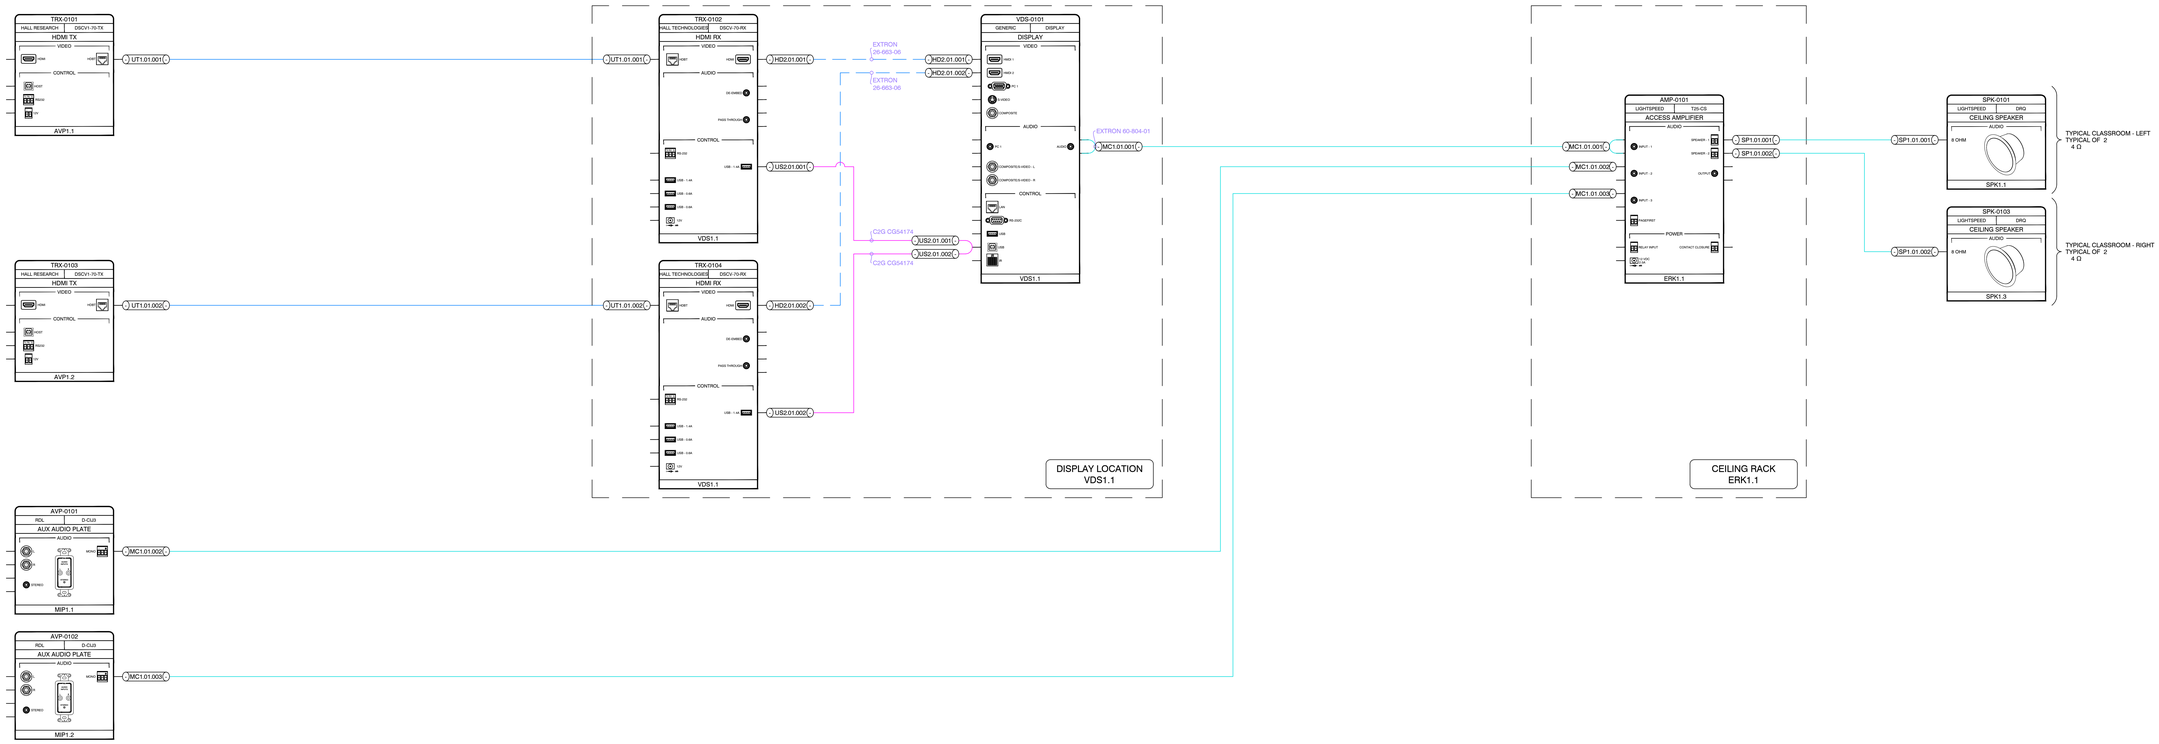

NUM	NOTES
1	-
2	-
3	-
4	-
5	-
6	-
7	-

LINE DESIGNATIONS KEY

- BULK - AUDIO
- PATCH - AUDIO
- BULK - VIDEO
- PATCH - VIDEO
- BULK - CONTROL
- PATCH - CONTROL
- BULK - GENERIC
- PATCH - GENERIC

MARSHALL INDUSTRIES

www.marshallind.com

PROJECT INFORMATION

5795

SALEM HILLS HS

FIELD HOUSE AV/TCU- NSD

CUSTOMER NAME: NEBO UT SCHOOL DISTRICT	CUSTOMER NUMBER: 1699
SITE NAME: SALEM HILLS HIGH SCHOOL	SITE NUMBER: 122928

SITE ADDRESS:
200 NORTH MAIN STREET
SALEM, UT 84653

SALES PERSON: MALISA TROUTWINE	ENGINEERED BY: MIKE PLATTNER
DRAFTER: ELI ANDERSON	PROJECT MANAGER: BRETT MELI

DRAWING SET INFORMATION

PHASE: CONSTRUCTION

PUBLISH DATE: 1/14/2026

PLOT SIZE: ARCH FULL BLEED E (36.00 X 48.00 INCHES)

PLOT SCALE: 1' = 1'-0"

APPROVED BY: -----

SHEET REVISION INFORMATION

REVISION:	REVISION DATE:
----	REVISION DESCRIPTION: -----

REVISION & ISSUE HISTORY

ISSUED FOR:	REV.	DATE:
---	---	---
---	---	---
SALEM HILLS HS

SINGLE LINE DIAGRAMS

TYPICALCLASSROOM

SYSTEM FUNCTIONAL

AV801.1

FILE NAME: AV800.DWG

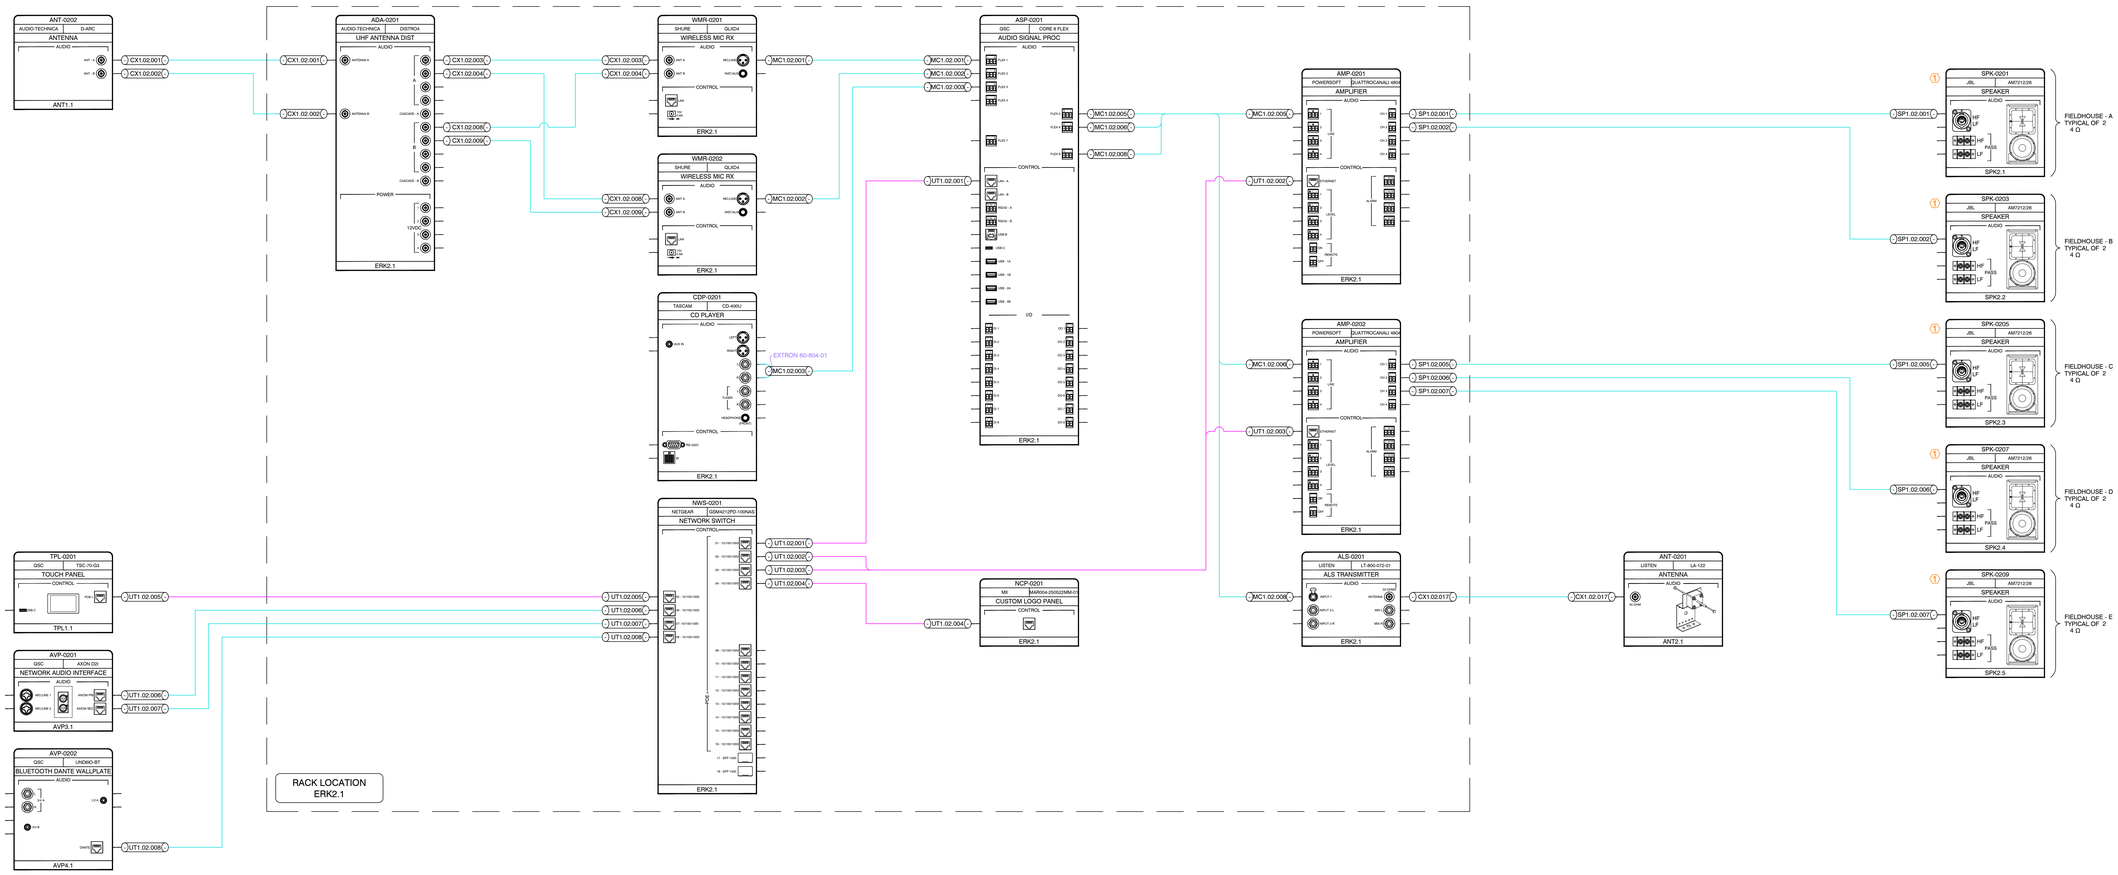

NUM	NOTES
1	MOUNT WITH JBL MTU-3
2	-
3	-
4	-
5	-
6	-
7	-

LINE DESIGNATIONS KEY

- BULK - AUDIO
- PATCH - AUDIO
- BULK - VIDEO
- PATCH - VIDEO
- BULK - CONTROL
- PATCH - CONTROL
- BULK - GENERIC
- PATCH - GENERIC

MARSHALL INDUSTRIES

www.marshallind.com

PROJECT INFORMATION

5795

SALEM HILLS HS

FIELD HOUSE AV/TCU- NSD

CUSTOMER NAME: NEBO UT SCHOOL DISTRICT	CUSTOMER NUMBER: 1699
SITE NAME: SALEM HILLS HIGH SCHOOL	SITE NUMBER: 122928

SITE ADDRESS:
200 NORTH MAIN STREET
SALEM, UT 84653

SALES PERSON: MALISA TROUTWINE	ENGINEERED BY: MIKE PLATTNER
DRAFTER: ELI ANDERSON	PROJECT MANAGER: BRETT MELI

DRAWING SET INFORMATION

PHASE: CONSTRUCTION

PUBLISH DATE: 1/14/2026

PLOT SIZE: ARCH FULL BLEED E (36.00 X 48.00 INCHES)

PLOT SCALE: 1' = 1'-0"

APPROVED BY: -----

SHEET REVISION INFORMATION

REVISION:	REVISION DATE:	REVISION DESCRIPTION:
----	-----	-----

REVISION & ISSUE HISTORY

ISSUED FOR:	REV.	DATE:
---	---	---
---	---	---
SALEM HILLS HS

SINGLE LINE DIAGRAMS

FIELDHOUSE

SYSTEM FUNCTIONAL

AV802.1

FILE NAME: AV800.DWG

ERK-0201

18RU WALL RACK

18	RESOLUT / MARSHALL INDUSTRIES	
17	LISTEN ALS-0201 LT-800-072-01	
16	AUDIO-TECHNICA ADA-0201 DISTRO4	
15	SHURE WMR-0201 QLXD4	SHURE WMR-0202 QLXD4
14	1RU BLANK	
13	NETGEAR NWS-0201 GSM4212PD-100NAS	
12	OSC ASP-0201 CORE 8 FLEX	
11	1RU BLANK	
10	TASCAM CDP-0201 CD-400U	
09	1RU BLANK	
08	MIDDLE ATLANTIC 2RU LOCKING DRAWER D2LK	
07		
06	2RU BLANK	
05		
04	POWERSOFT AMP-0201 QUATTROCANALI 4804	
03	1RU BLANK	
02	POWERSOFT AMP-0202 QUATTROCANALI 4804	
01	FURMAN ACC-0205 PL-PRO DMC	

MIDDLE ATLANTIC ERK2.1 DWR-18-22PD

1 **ERK2.1**
SCALE: 3" = 1'-0"

MARSHALL INDUSTRIES

www.marshallind.com

PROJECT INFORMATION

5795

SALEM HILLS HS

FIELD HOUSE AV/TCU- NSD

CUSTOMER NAME: NEBO UT SCHOOL DISTRICT	CUSTOMER NUMBER: 1699
SITE NAME: SALEM HILLS HIGH SCHOOL	SITE NUMBER: 122928
SITE ADDRESS: 200 NORTH MAIN STREET SALEM, UT 84653	
SALES PERSON: MALISA TROUTWINE	ENGINEERED BY: MIKE PLATTNER
DRAFTER: ELI ANDERSON	PROJECT MANAGER: BRETT MELI

DRAWING SET INFORMATION

PHASE: CONSTRUCTION

PUBLISH DATE: 1/14/2026

PLOT SIZE: ARCH FULL BLEED E (36.00 X 48.00 INCHES)

PLOT SCALE: 1' = 1'-0"

APPROVED BY: -----

SHEET REVISION INFORMATION

REVISION:	REVISION DATE:	
----	REVISION DESCRIPTION:	-----

REVISION & ISSUE HISTORY

ISSUED FOR:	REV.	DATE:
---	---	---
---	---	---
SALEM HILLS HS

ENCLOSURE ELEVATIONS

UTILIZED RACKS

AV901

FILE NAME: AV900.DWG

INTERCOM LEGEND

SYM	MAKE	MODEL	DESCRIPTION	BACK BOX
CLK	AMERICAN TIME	E96BAGD304	12" CLOCK	
CLK	AMERICAN TIME	E96BAGD304	19" ALLSET AUTO DST ADJUSTMENT	
CS	RAULAND	TCC2211PB	CALL SWITCH RJ45 EMER CHECK-IN	1 GANG 3" DEEP BACKBOX AT SWITCH HEIGHT
CS	QUAM	SYSTEM 1	IKOPAK LOUDSPEAKER	
CS	RAULAND	BAPKIT1X25IRJ	8 OHM 1X2 SPKR ASSY W/RJ45	
SPK	ATLAS SOUND	SD72	8" DUAL CONE SPEAKER W/ 25V/70V 5-WATT TRANSFORMER	CP67
SPK	ATLAS SOUND	SD70W	8" DUAL CONE IN-CEILING SPEAKER	
SPK	ATLAS SOUND	VTF-15UCN	OUTSIDE SPEAKER	4SQ. BACK BOX AND RACO 301 EXTENSION RING.
25/65	WEST PENN	25365B	22AWG - 2 SHLD, 2 UNSHLD INTERCOM CABLE	
CAT6	CIG	CG27196	50FT CAT6 SNAGLESS UTP CABLE-YLW	

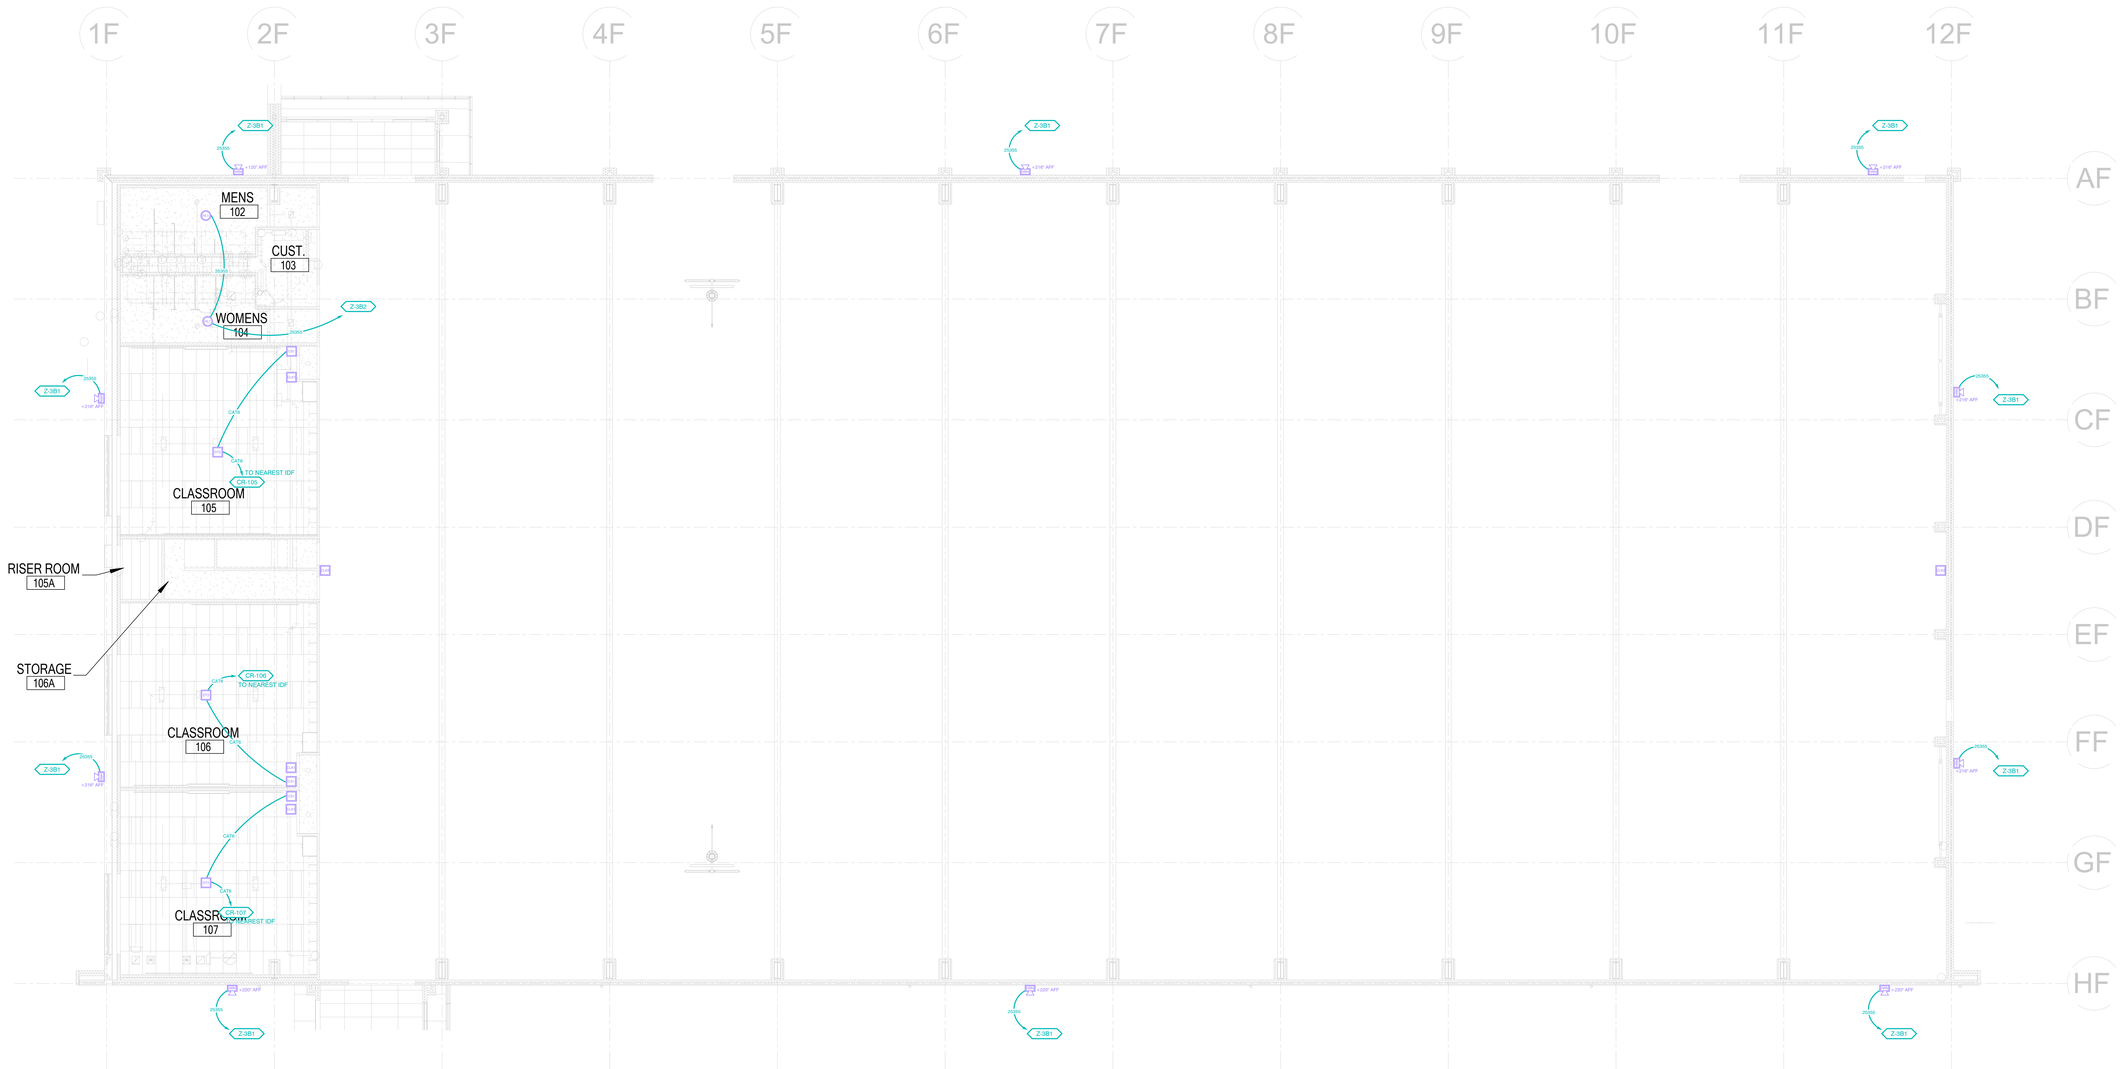

MARSHALL INDUSTRIES

www.marshallind.com

PROJECT INFORMATION

5795

SALEM HILLS HS

FIELD HOUSE AV/TCU- NSD

CUSTOMER NAME: NEBO UT SCHOOL DISTRICT	CUSTOMER NUMBER: 1699
SITE NAME: SALEM HILLS HIGH SCHOOL	SITE NUMBER: 122928

SITE ADDRESS:
200 NORTH MAIN STREET
SALEM, UT 84653

SALES PERSON: MALISA TROUTWINE	ENGINEERED BY: MIKE PLATTNER
DRAFTER: ELI ANDERSON	PROJECT MANAGER: BRETT MELI

DRAWING SET INFORMATION

PHASE: CONSTRUCTION

PUBLISH DATE: 1/14/2026

PLOT SIZE: ARCH FULL BLEED E (36.00 X 48.00 INCHES)

PLOT SCALE: 1" = 1'-0"

APPROVED BY: -----

SHEET REVISION INFORMATION

REVISION:	REVISION DATE:
----	REVISION DESCRIPTION: -----

REVISION & ISSUE HISTORY

ISSUED FOR:	REV.	DATE:
---	---	---
---	---	---
SALEM HILLS HS

INTERCOMMUNICATION

MAIN LEVEL

IC101

FILE NAME: AV100.DWG

INTERCOM LEGEND				
SYM	MAKE	MODEL	DESCRIPTION	BACK BOX
12"	AMERICAN TIME	E96BAQC004	12" CLOCK	
12"	AMERICAN TIME	E96BAQD004	10" ALLSET AUTO DST ADJUSTMENT	
CF	RAULAND	TCC2211PB	CALL SWITCH RJ45 EMER CHECK-IN	1 GANG 3" DEEP BACKBOX AT SWITCH HEIGHT
CS	QUAM	SYSTEM 1	IKOPAK LOUDSPEAKER	
CS	RAULAND	BAPKIT1K25RJ	8 CHM 1X2 SPKR ASSY W/RJ45	
SM	ATLAS SOUND	SD72	8" DUAL CONE SPEAKER W/ 25V/70V 5-WATT TRANSFORMER	CPR7
S	ATLAS SOUND	SD72W	8" DUAL CONE IN-CEILING SPEAKER	
SOS	ATLAS SOUND	VTF-15UCN	OUTSIDE SPEAKER	4SQ. BACK BOX AND RACO 201 EXTENSION RING.
25395'	WEST PENN	25395B	22AWG - 2 SHLD, 2 LNGHLD INTERCOM CABLE	
CAT6'	CIG	CG27196	50FT CAT6 SNAGLESS UTP CABLE-YLW	

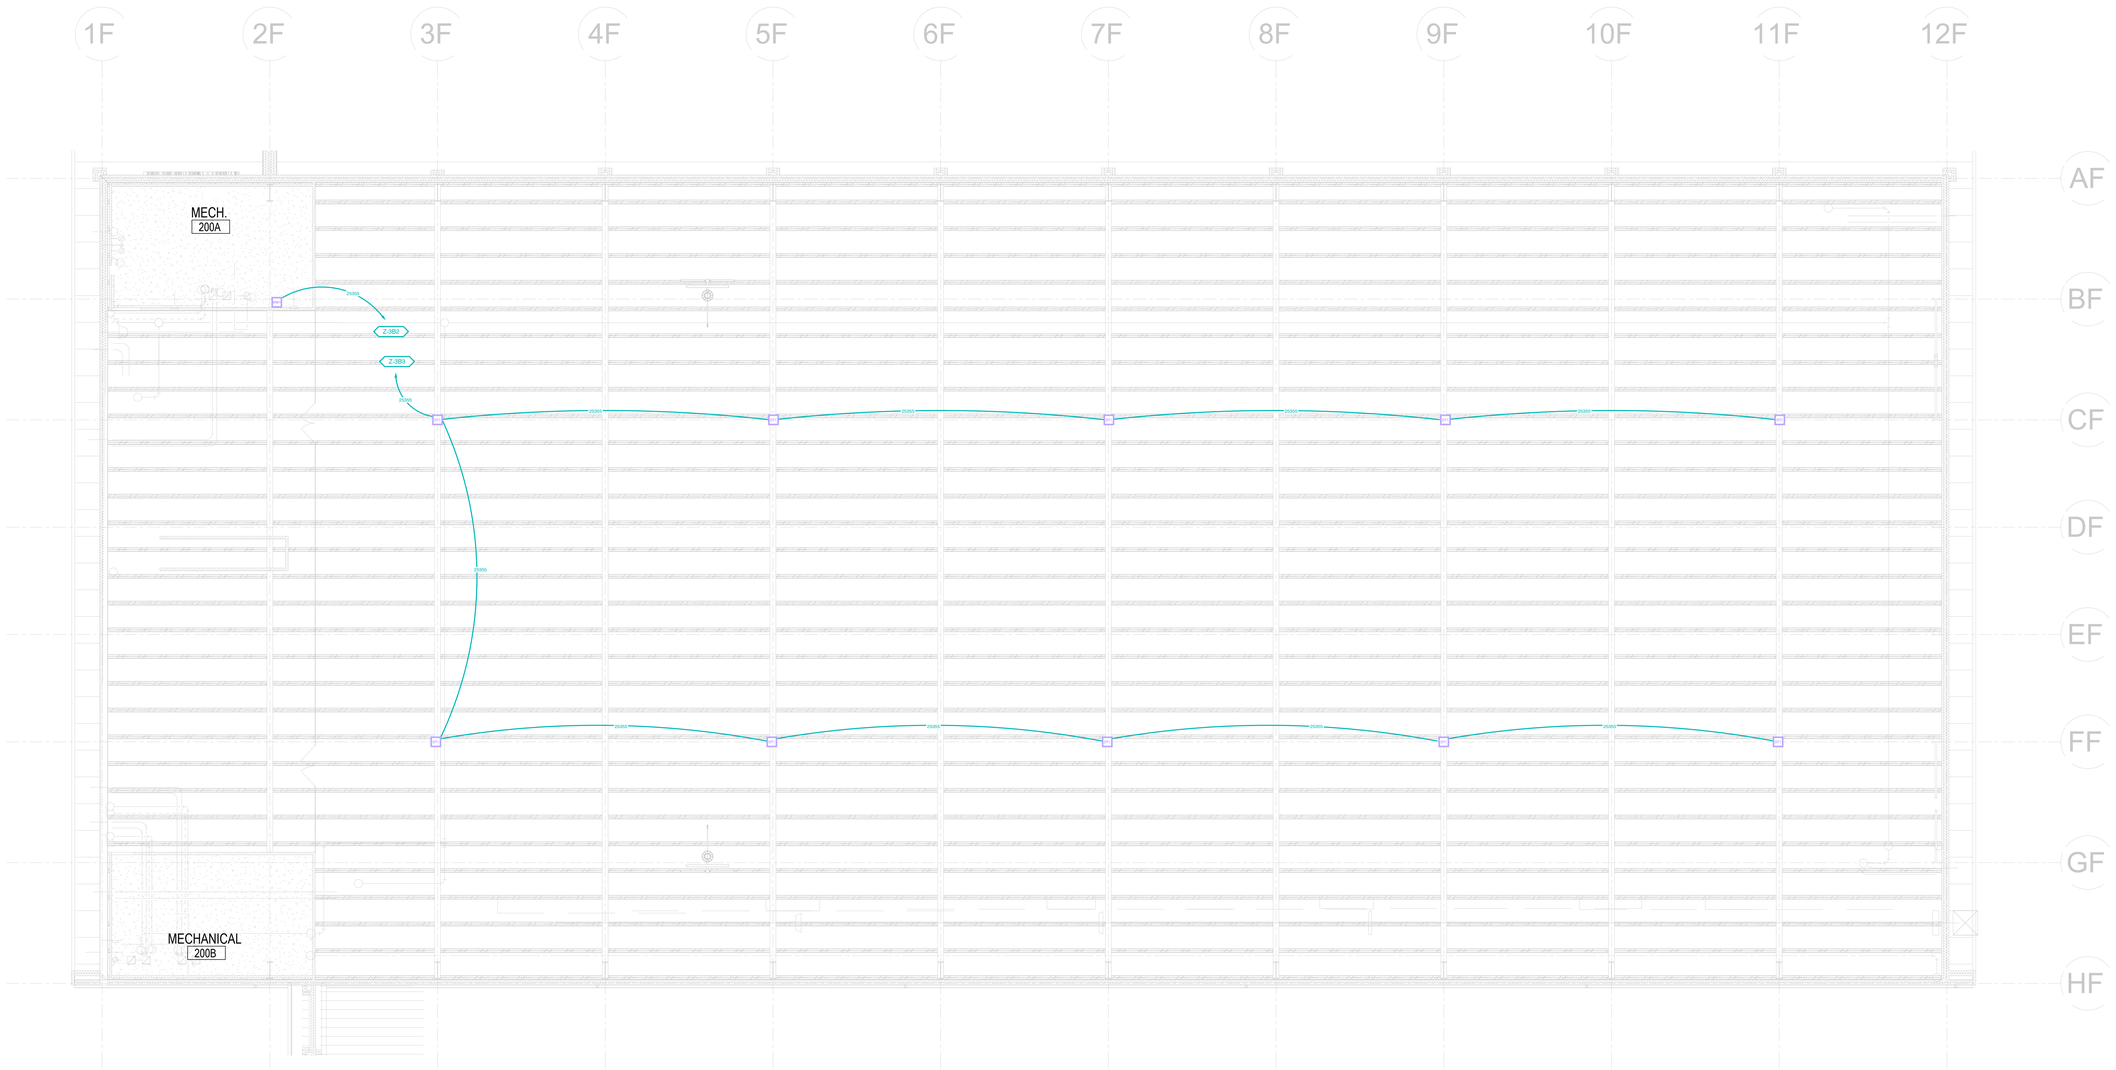

MARSHALL INDUSTRIES

www.marshallind.com

PROJECT INFORMATION

5795

SALEM HILLS HS

FIELD HOUSE AV/TCU- NSD

CUSTOMER NAME: NEBO UT SCHOOL DISTRICT	CUSTOMER NUMBER: 1699
SITE NAME: SALEM HILLS HIGH SCHOOL	SITE NUMBER: 122928

SITE ADDRESS:
200 NORTH MAIN STREET
SALEM, UT 84653

SALES PERSON: MALISA TROUTWINE	ENGINEERED BY: MIKE PLATTNER
DRAFTER: ELI ANDERSON	PROJECT MANAGER: BRETT MELI

DRAWING SET INFORMATION

PHASE: CONSTRUCTION

PUBLISH DATE: 1/14/2026

PLOT SIZE: ARCH FULL BLEED E (36.00 X 48.00 INCHES)

PLOT SCALE: 1" = 1'-0"

APPROVED BY: -----

SHEET REVISION INFORMATION

REVISION:	REVISION DATE:
----	REVISION DESCRIPTION: -----

REVISION & ISSUE HISTORY

ISSUED FOR:	REV.	DATE:
---	---	---
---	---	---
SALEM HILLS HS

INTERCOMMUNICATION

SECOND LEVEL

IC102

FILE NAME: AV100.DWG

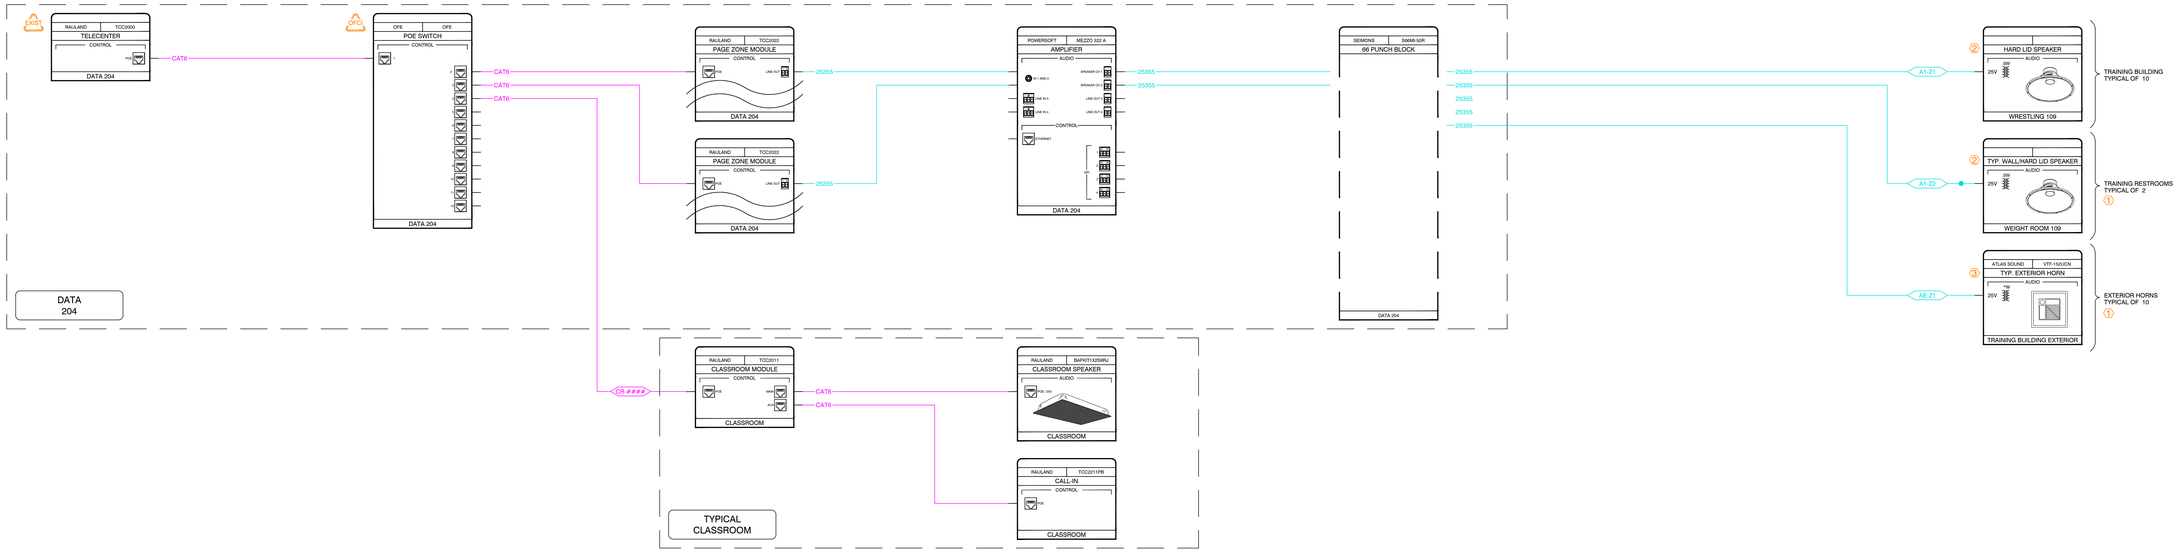

NUM	NOTES
1	SPEAKER TYPES IN ZONE MAY VARY. VERIFY EXACT SPEAKER TYPES IN ZONE ON SHEET IC202.A AND TAP ACCORDING TO COVERAGE AREA SIZE.
2	HARD LID SPEAKERS REQUIRE A LOWELL P875X-4 BACK BOX.
3	TYPICAL HORNS REQUIRE 4SQ. BACK BOX AND RACO 201 EXTENSION RING.
4	-
5	-
6	-
7	-

LINE DESIGNATIONS KEY

- BULK - AUDIO
- PATCH - AUDIO
- BULK - VIDEO
- PATCH - VIDEO
- BULK - CONTROL
- PATCH - CONTROL
- BULK - GENERIC
- PATCH - GENERIC

MARSHALL INDUSTRIES

www.marshallind.com

PROJECT INFORMATION

5795

SALEM HILLS HS

FIELD HOUSE AV/TCU- NSD

CUSTOMER NAME: NEBO UT SCHOOL DISTRICT	CUSTOMER NUMBER: 1699
SITE NAME: SALEM HILLS HIGH SCHOOL	SITE NUMBER: 122928
SITE ADDRESS: 200 NORTH MAIN STREET SALEM, UT 84653	
SALES PERSON: MALISA TROUTWINE	ENGINEERED BY: MIKE PLATTNER
DRAFTER: ELI ANDERSON	PROJECT MANAGER: BRETT MELI

DRAWING SET INFORMATION

PHASE: CONSTRUCTION

PUBLISH DATE: 1/14/2026

PLOT SIZE: ARCH FULL BLEED E (36.00 X 48.00 INCHES)

PLOT SCALE: 1' = 1'-0"

APPROVED BY: -----

SHEET REVISION INFORMATION

REVISION:	REVISION DATE: -----
----	REVISION DESCRIPTION: -----

REVISION & ISSUE HISTORY

ISSUED FOR:	REV.	DATE:
---	---	---
---	---	---
SALEM HILLS HS

INTERCOMMUNICATION

GENERIC TCU RISER

IC801.1

FILE NAME: IC801.DWG